


Pérgola y cochera — ángulos 3D

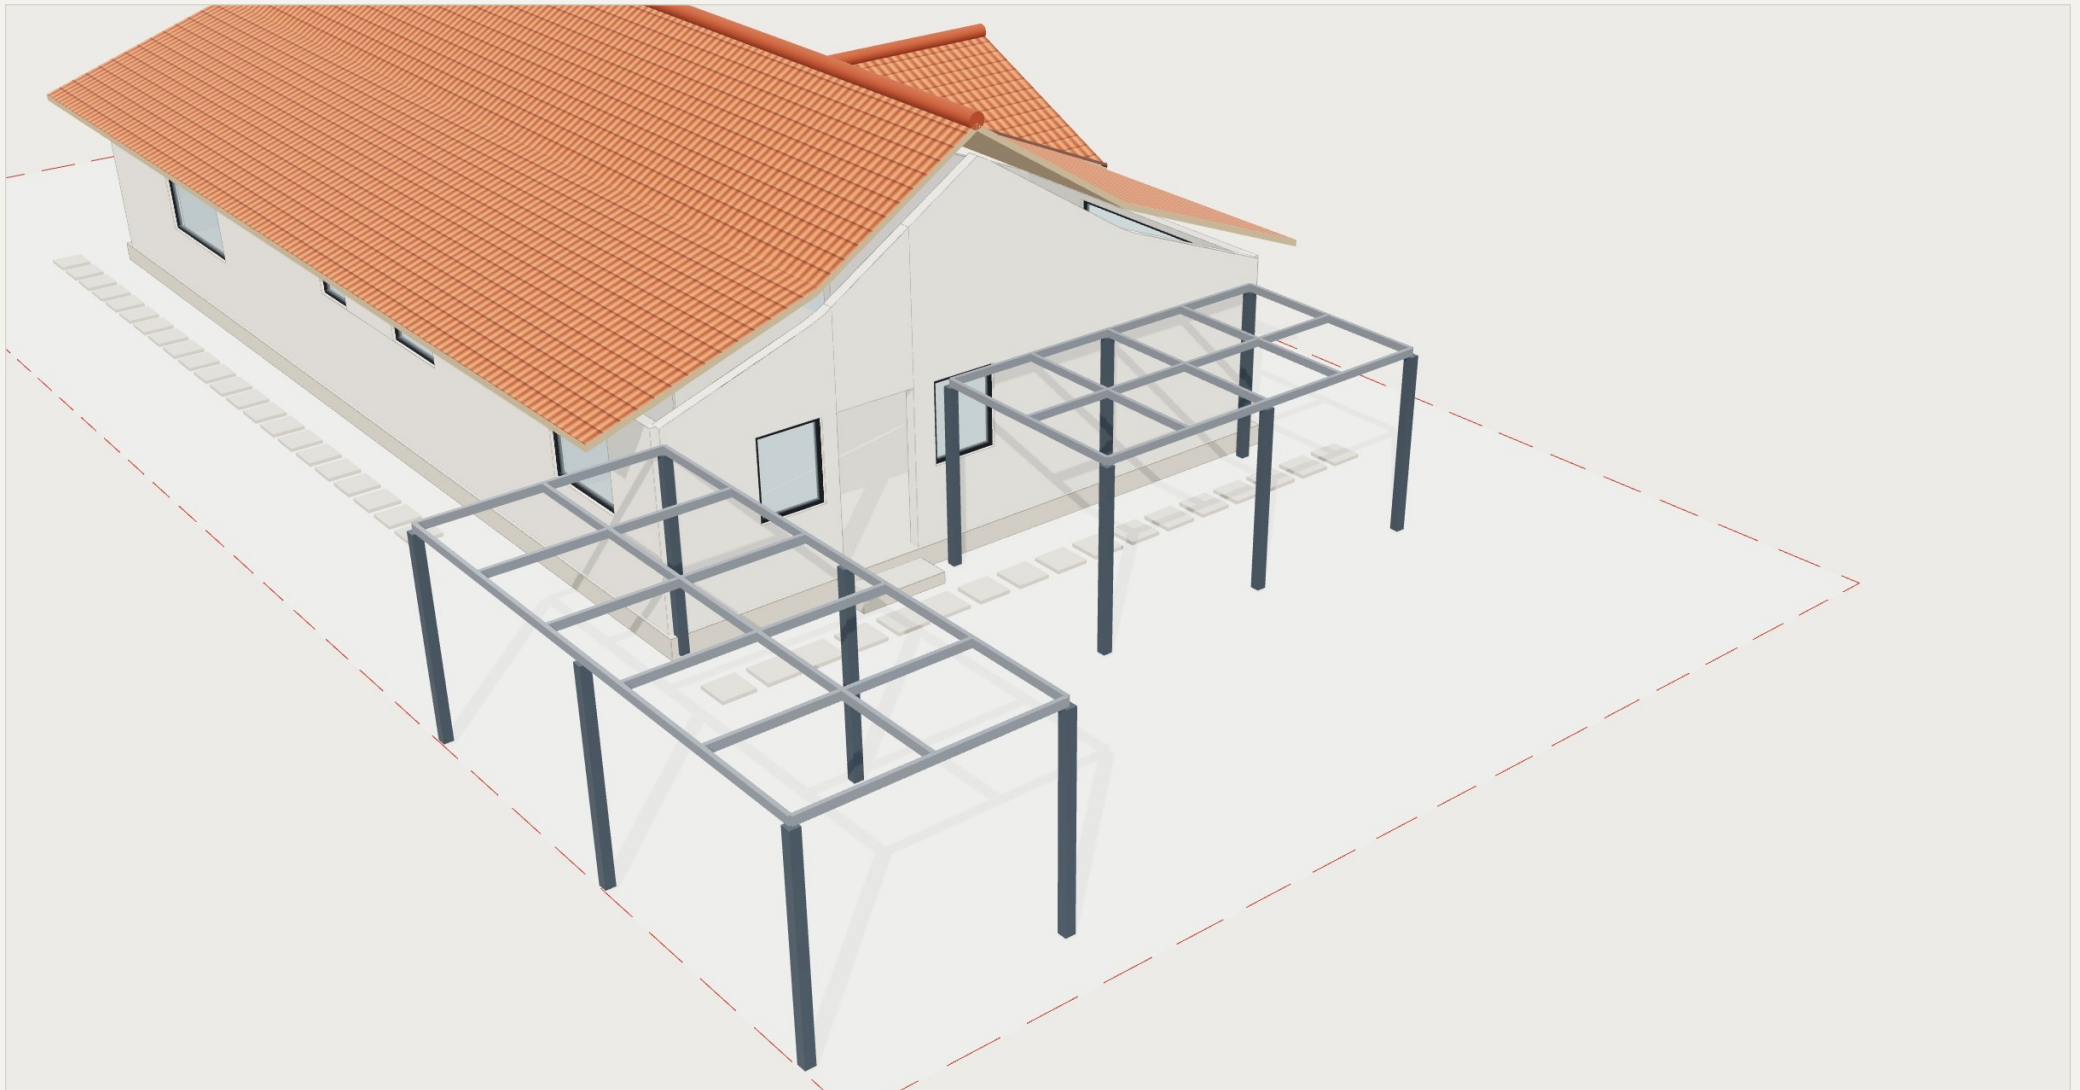

VISTA GENERAL. Cochera de $6,81 \times 2,93$ m y pérgola de $4,86 \times 2,80$ m. La casa aparece terminada, solo como contexto.

Columnas · 12

Tubo cuad. $120 \times 120 \times 4$ mm


Vigas · 20

Tubo rect. $100 \times 50 \times 2,5$ mm

Uniones soldadas

35 nodos en las dos estructuras

Cochera y pérgola — columnas y vigas

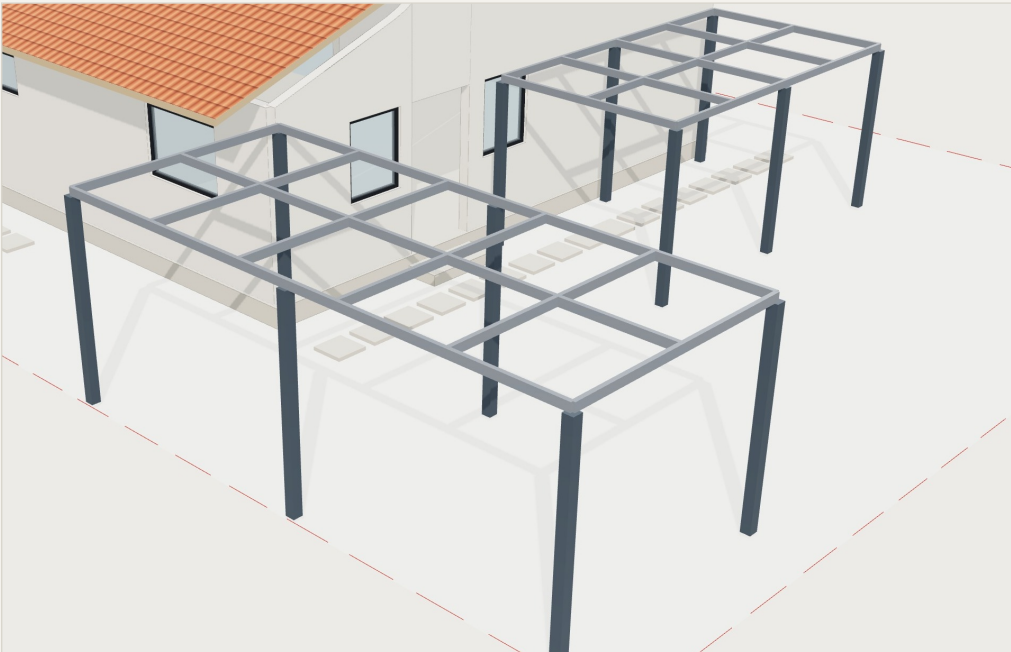


COCHERA — 6,81 × 2,93 m. 5 vanos, eje central continuo.

Cochera · 6,81 × 2,93 m

altura de columna 2,55 m (referencia)

PIEZA	TUBO (mm)	CANT.	m	kg
Columnas	120×120×4	6	15,00	219
Largueros	100×50×2,5	2	13,62	77
Cabezales	100×50×2,5	2	5,86	33
Travesaños	100×50×2,5	4	11,72	67
Eje central	100×50×2,5	1	6,81	39
Subtotal		15	53,01	435

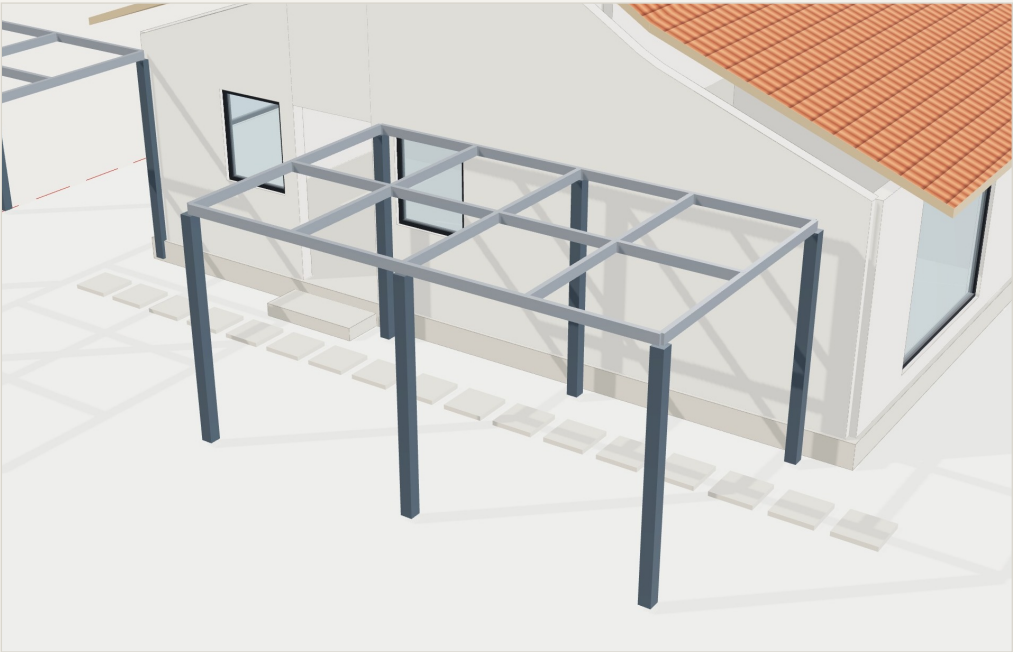

PÉRGOLA — 4,86 × 2,80 m. 4 vanos, eje central en 4 tramos.

Pérgola · 4,86 × 2,80 m

altura de columna 2,40 m (referencia)

PIEZA	TUBO (mm)	CANT.	m	kg
Columnas	120×120×4	6	14,10	205
Largueros	100×50×2,5	2	9,72	55
Cabezales	100×50×2,5	2	5,60	32
Travesaños	100×50×2,5	3	8,40	48
Eje central	100×50×2,5	4	4,86	28
Subtotal		17	42,68	368

Total etapa 2	32 piezas	·	95,69 m	·	803 kg	·	35 nodos de soldadura
---------------	-----------	---	---------	---	--------	---	-----------------------

Perfiles y cantidad de piezas según boceto del ejecutor (25/09/2026). Alturas y posición en el lote son de referencia. Longitudes a ejes, sin desperdicio. Trabajo independiente de la cubierta de la casa (etapa 1), que se ejecuta primero y se cotiza por separado.